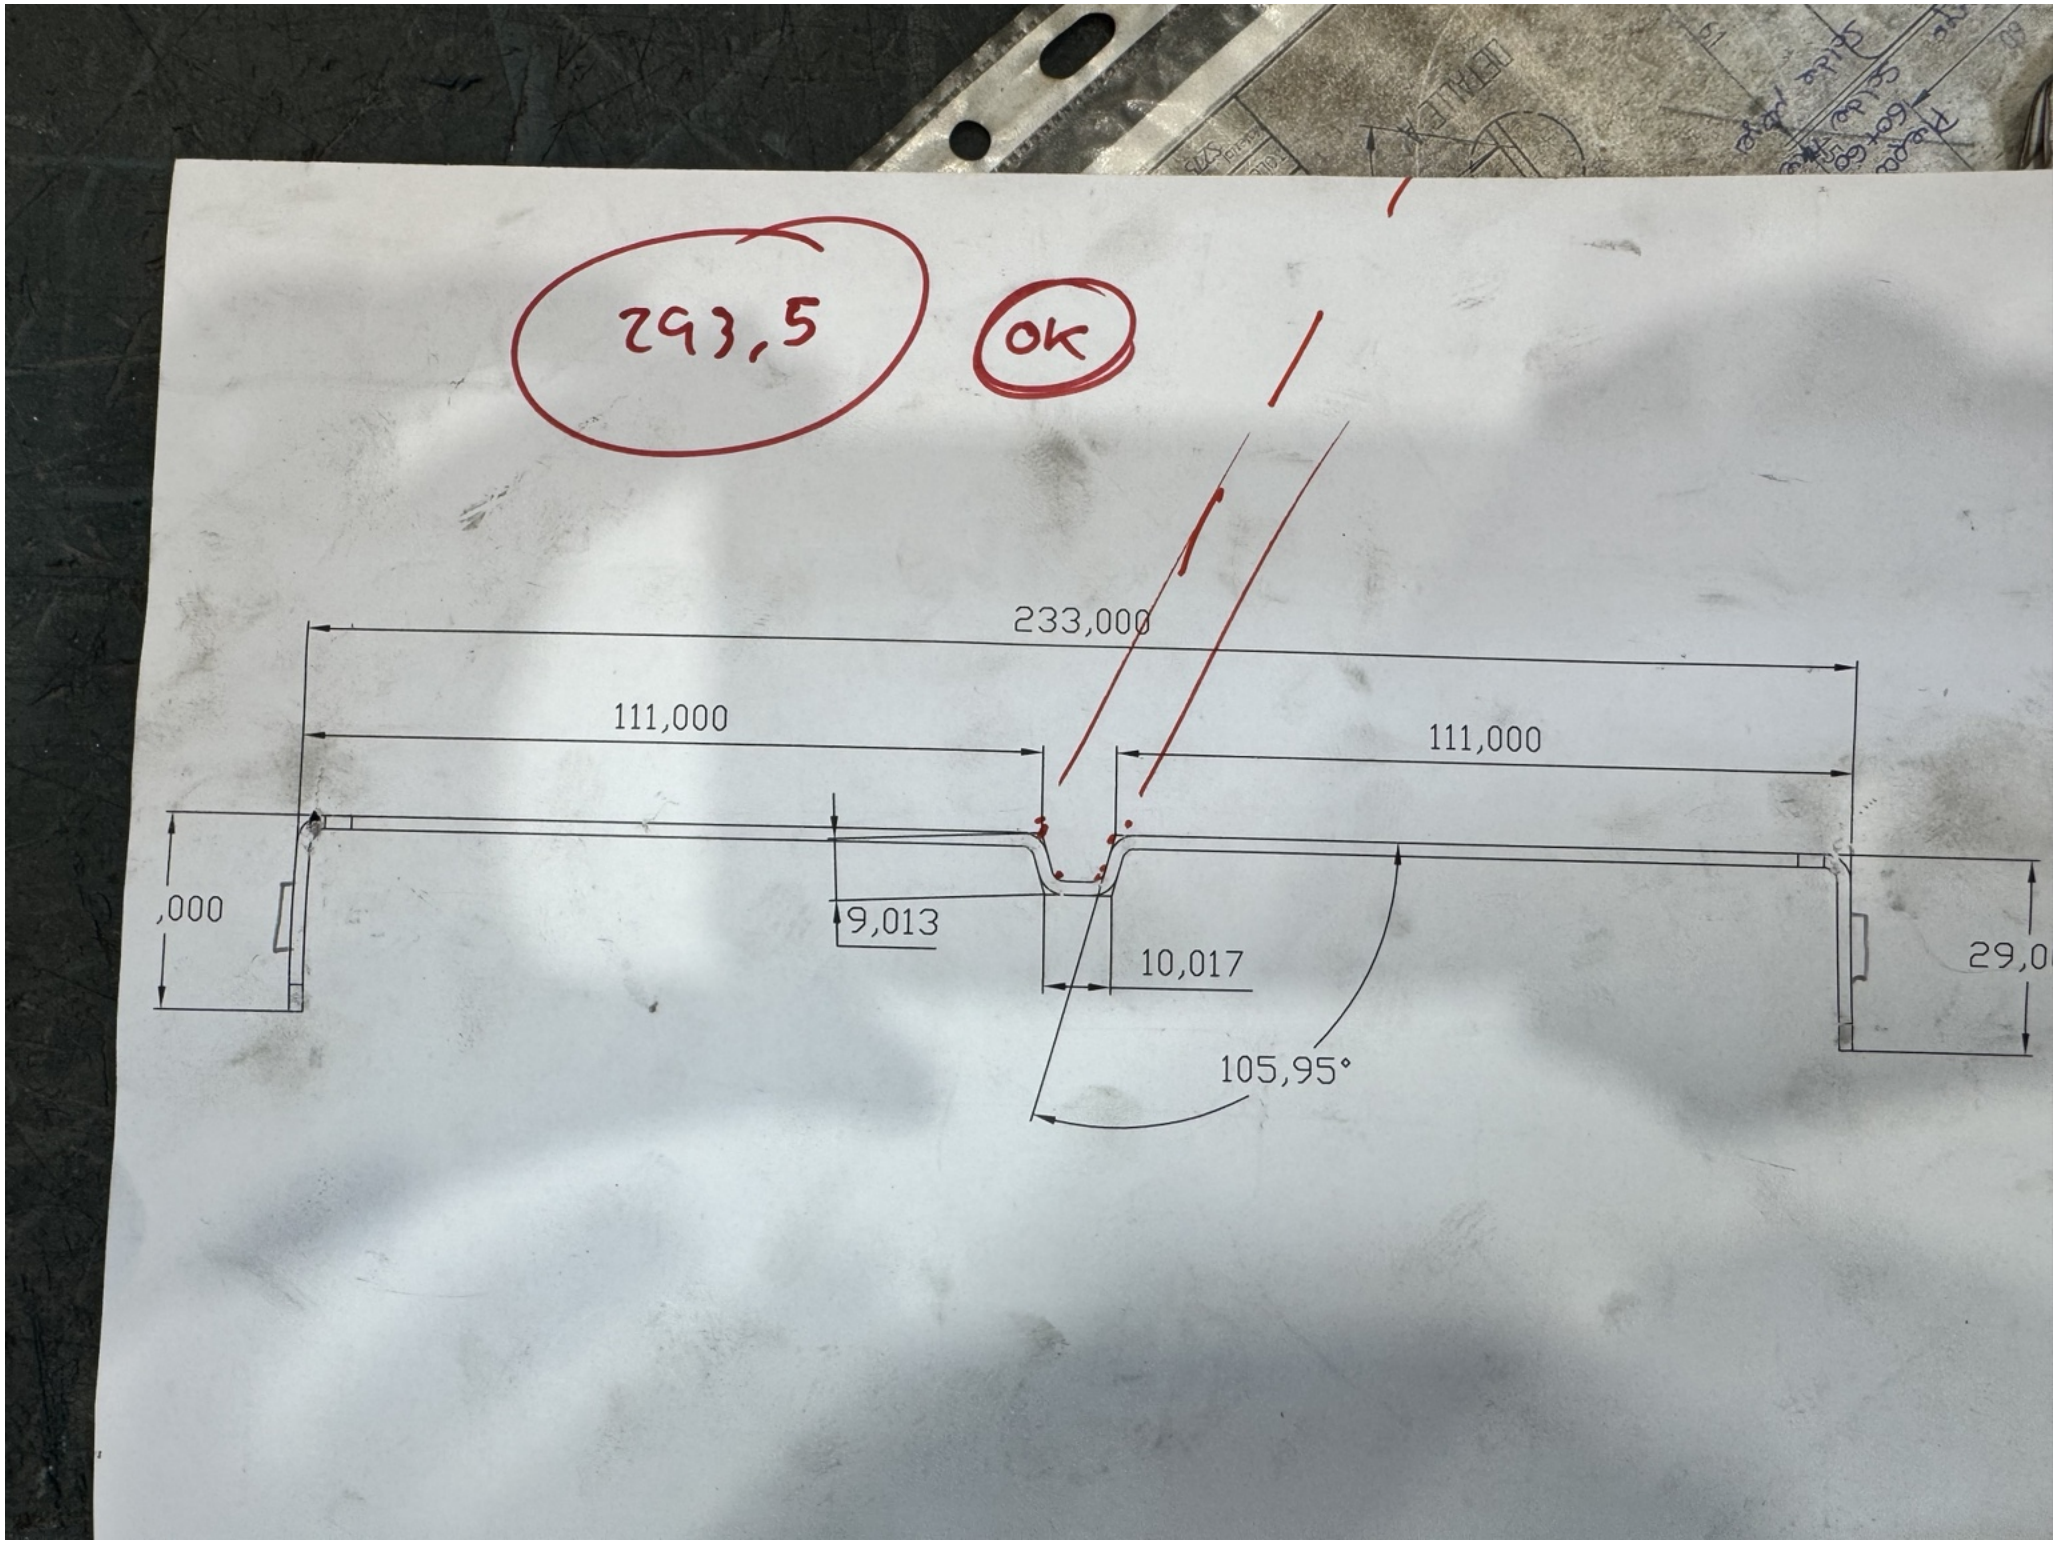

293,5
OK
233,000
111,000
111,000
,000
9,013
10,017
29,0
105,95°